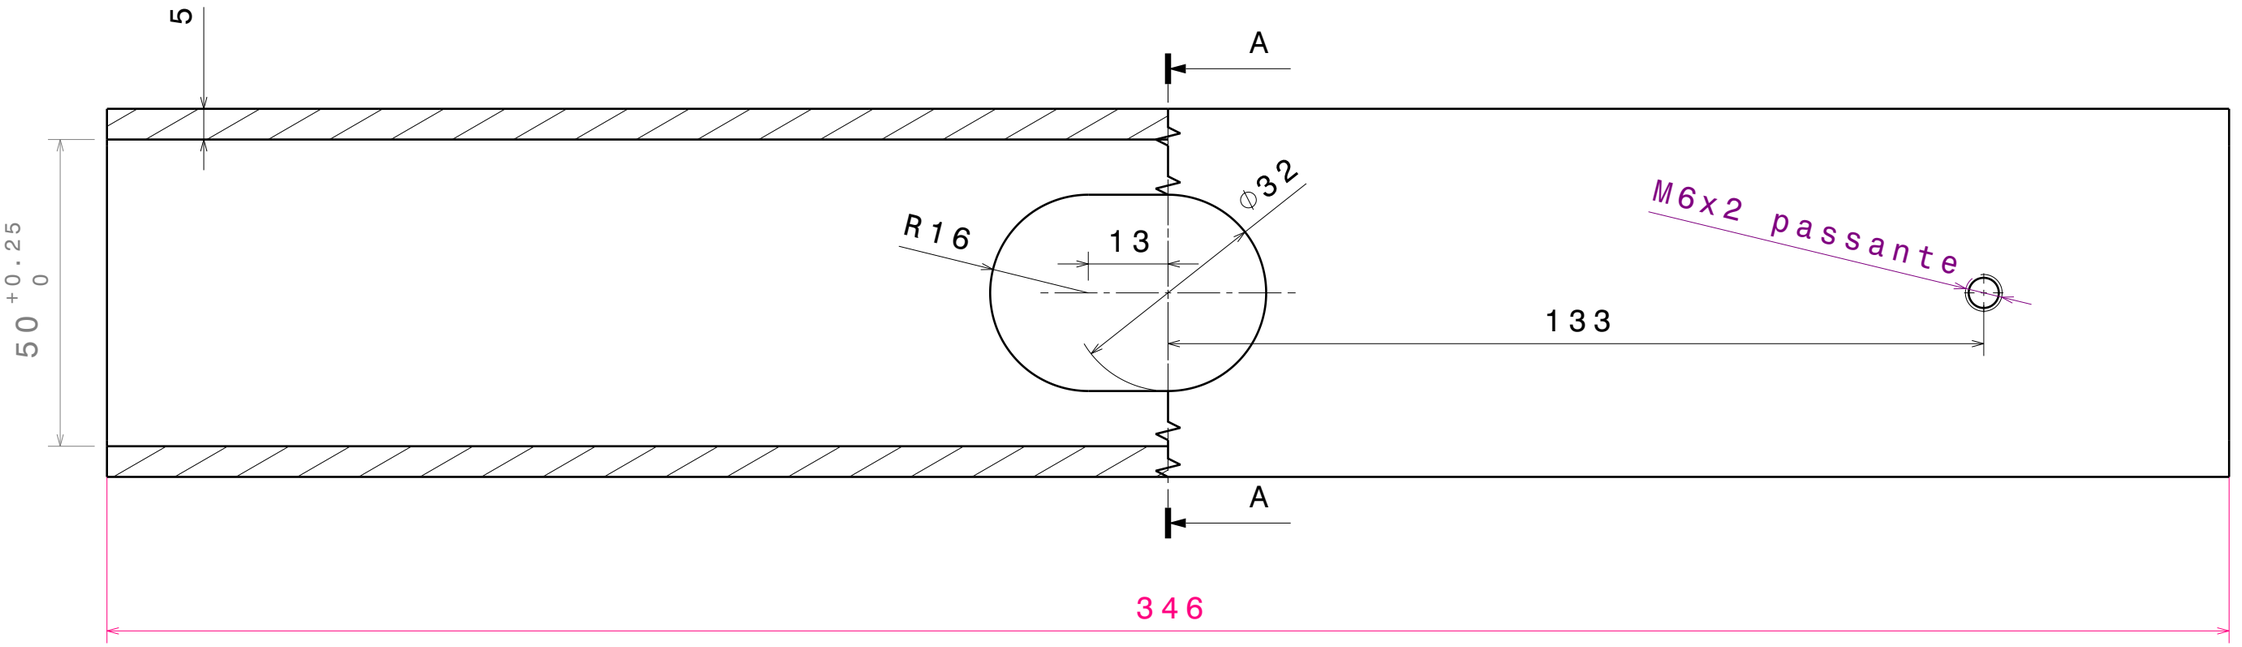

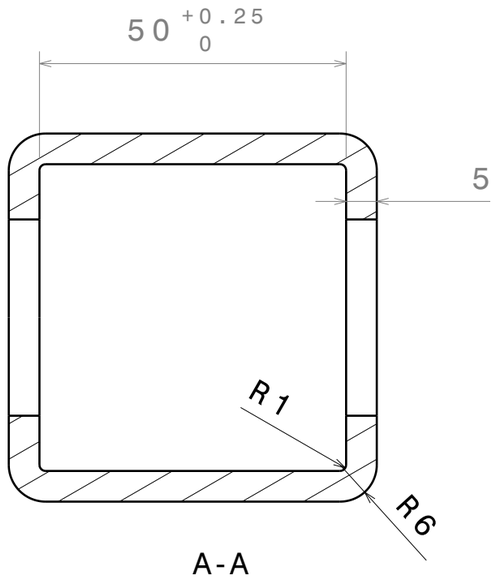

TOLL. GEN. ISO 2768, CLASSE: (fori +, alberi -):

Lineari: f Angolari: f Smussi e raccordi: f

Materiale: UNI-EN 10025 S235JR

3.2

Prova Finale		
MODEL NAME: **Tubolare**	DESIGNED BY: **Alessandro Lanza**	
DRAWING TITLE **Tubolare**	DRAWING AUTHOR: **Alessandro Lanza**	
DATE 05/09/2023	APPROVED BY:	POLITECNICO MILANO 1863
SCALE 1:1	SHEET SIZE: **A3**	